

VARUN A. SRIDHAR
2020BARC020

OPEN PARKING 2

EXHIBITION BUILDING
GROUND FLOOR PLAN

SCALE = 1:150

Architectural details include:

- Restrooms:** MEN'S RESTROOM (4600x3800), WOMEN'S RESTROOM (5600x3800), MEN'S RESTROOM (3600x4600), WOMEN'S RESTROOM (4600x3800).
- Exhibition Spaces:** OPEN EXHIBITS 1 (116 sqm), OPEN EXHIBITS 2 (10800x10000), AUDITORIUM (58.6 sqm).
- Support Spaces:** STORAGE ROOM (5800x9800), KITCHEN, ADMIN OFFICE (16600x13800), ADMIN CAFETERIA (9000x7000), SECURITY/CLOAK ROOM (5700x4600), TOILET COUNTER.
- Other Features:** BALCONY, PORTAL TUBE, BASEMENT ENTRY, BASEMENT EXIT, GATE A1 ENTRANCE, GATE A2 EXIT.
- Grid System:** Y1-Y6, XA-X5, Z1-Z3, UA-UB, ZD-ZE, ZA-ZC, UF-UE, UC.
- Dimensions:** Various room and overall building dimensions are provided in meters (e.g., 5800, 4400, 4600, 3866, 11100, 5530, 6300, 10500, 8000, 7000, 7106, 9400, 4500, 5900, 4400, 3200, 5000, 5000, 2100, 14100, 4000, 4000, 4000, 3600, 4800, 3200).

VARUN A. SRIDHAR
2020BARC020


OPEN PARKING 2

EXHIBITION BUILDING
GROUND FLOOR PLAN

SCALE = 1:150


Architectural details include:

- Restrooms:** MEN'S RESTROOM (4600x3800), WOMEN'S RESTROOM (5600x3800), MEN'S RESTROOM (3600x4600), WOMEN'S RESTROOM (4600x3800).
- Exhibition Spaces:** OPEN EXHIBITS 1 (116 sqm), OPEN EXHIBITS 2 (10800x10000), AUDITORIUM (58.6 sqm).
- Support Spaces:** STORAGE ROOM (5800x9800), KITCHEN, ADMIN OFFICE (16600x13800), ADMIN CAFETERIA (9000x7000), SECURITY/CLOAK ROOM (5700x4600), TOILET COUNTER.
- Other Features:** BALCONY, PORTAL TUBE, BASEMENT ENTRY, BASEMENT EXIT, GATE A1 ENTRANCE, GATE A2 EXIT.
- Grid System:** Y1-Y6, XA-X5, Z1-Z3, UA-UB, ZD-ZE, ZA-ZC, UF-UE, UC.
- Dimensions:** Various room and overall building dimensions are provided in meters (e.g., 5800, 4400, 4600, 3866, 11100, 5530, 6300, 10500, 8000, 7000, 7106, 9400, 4500, 5900, 4400, 3200, 5000, 5000, 2100, 14100, 4000, 4000, 3000, 4800, 4000).

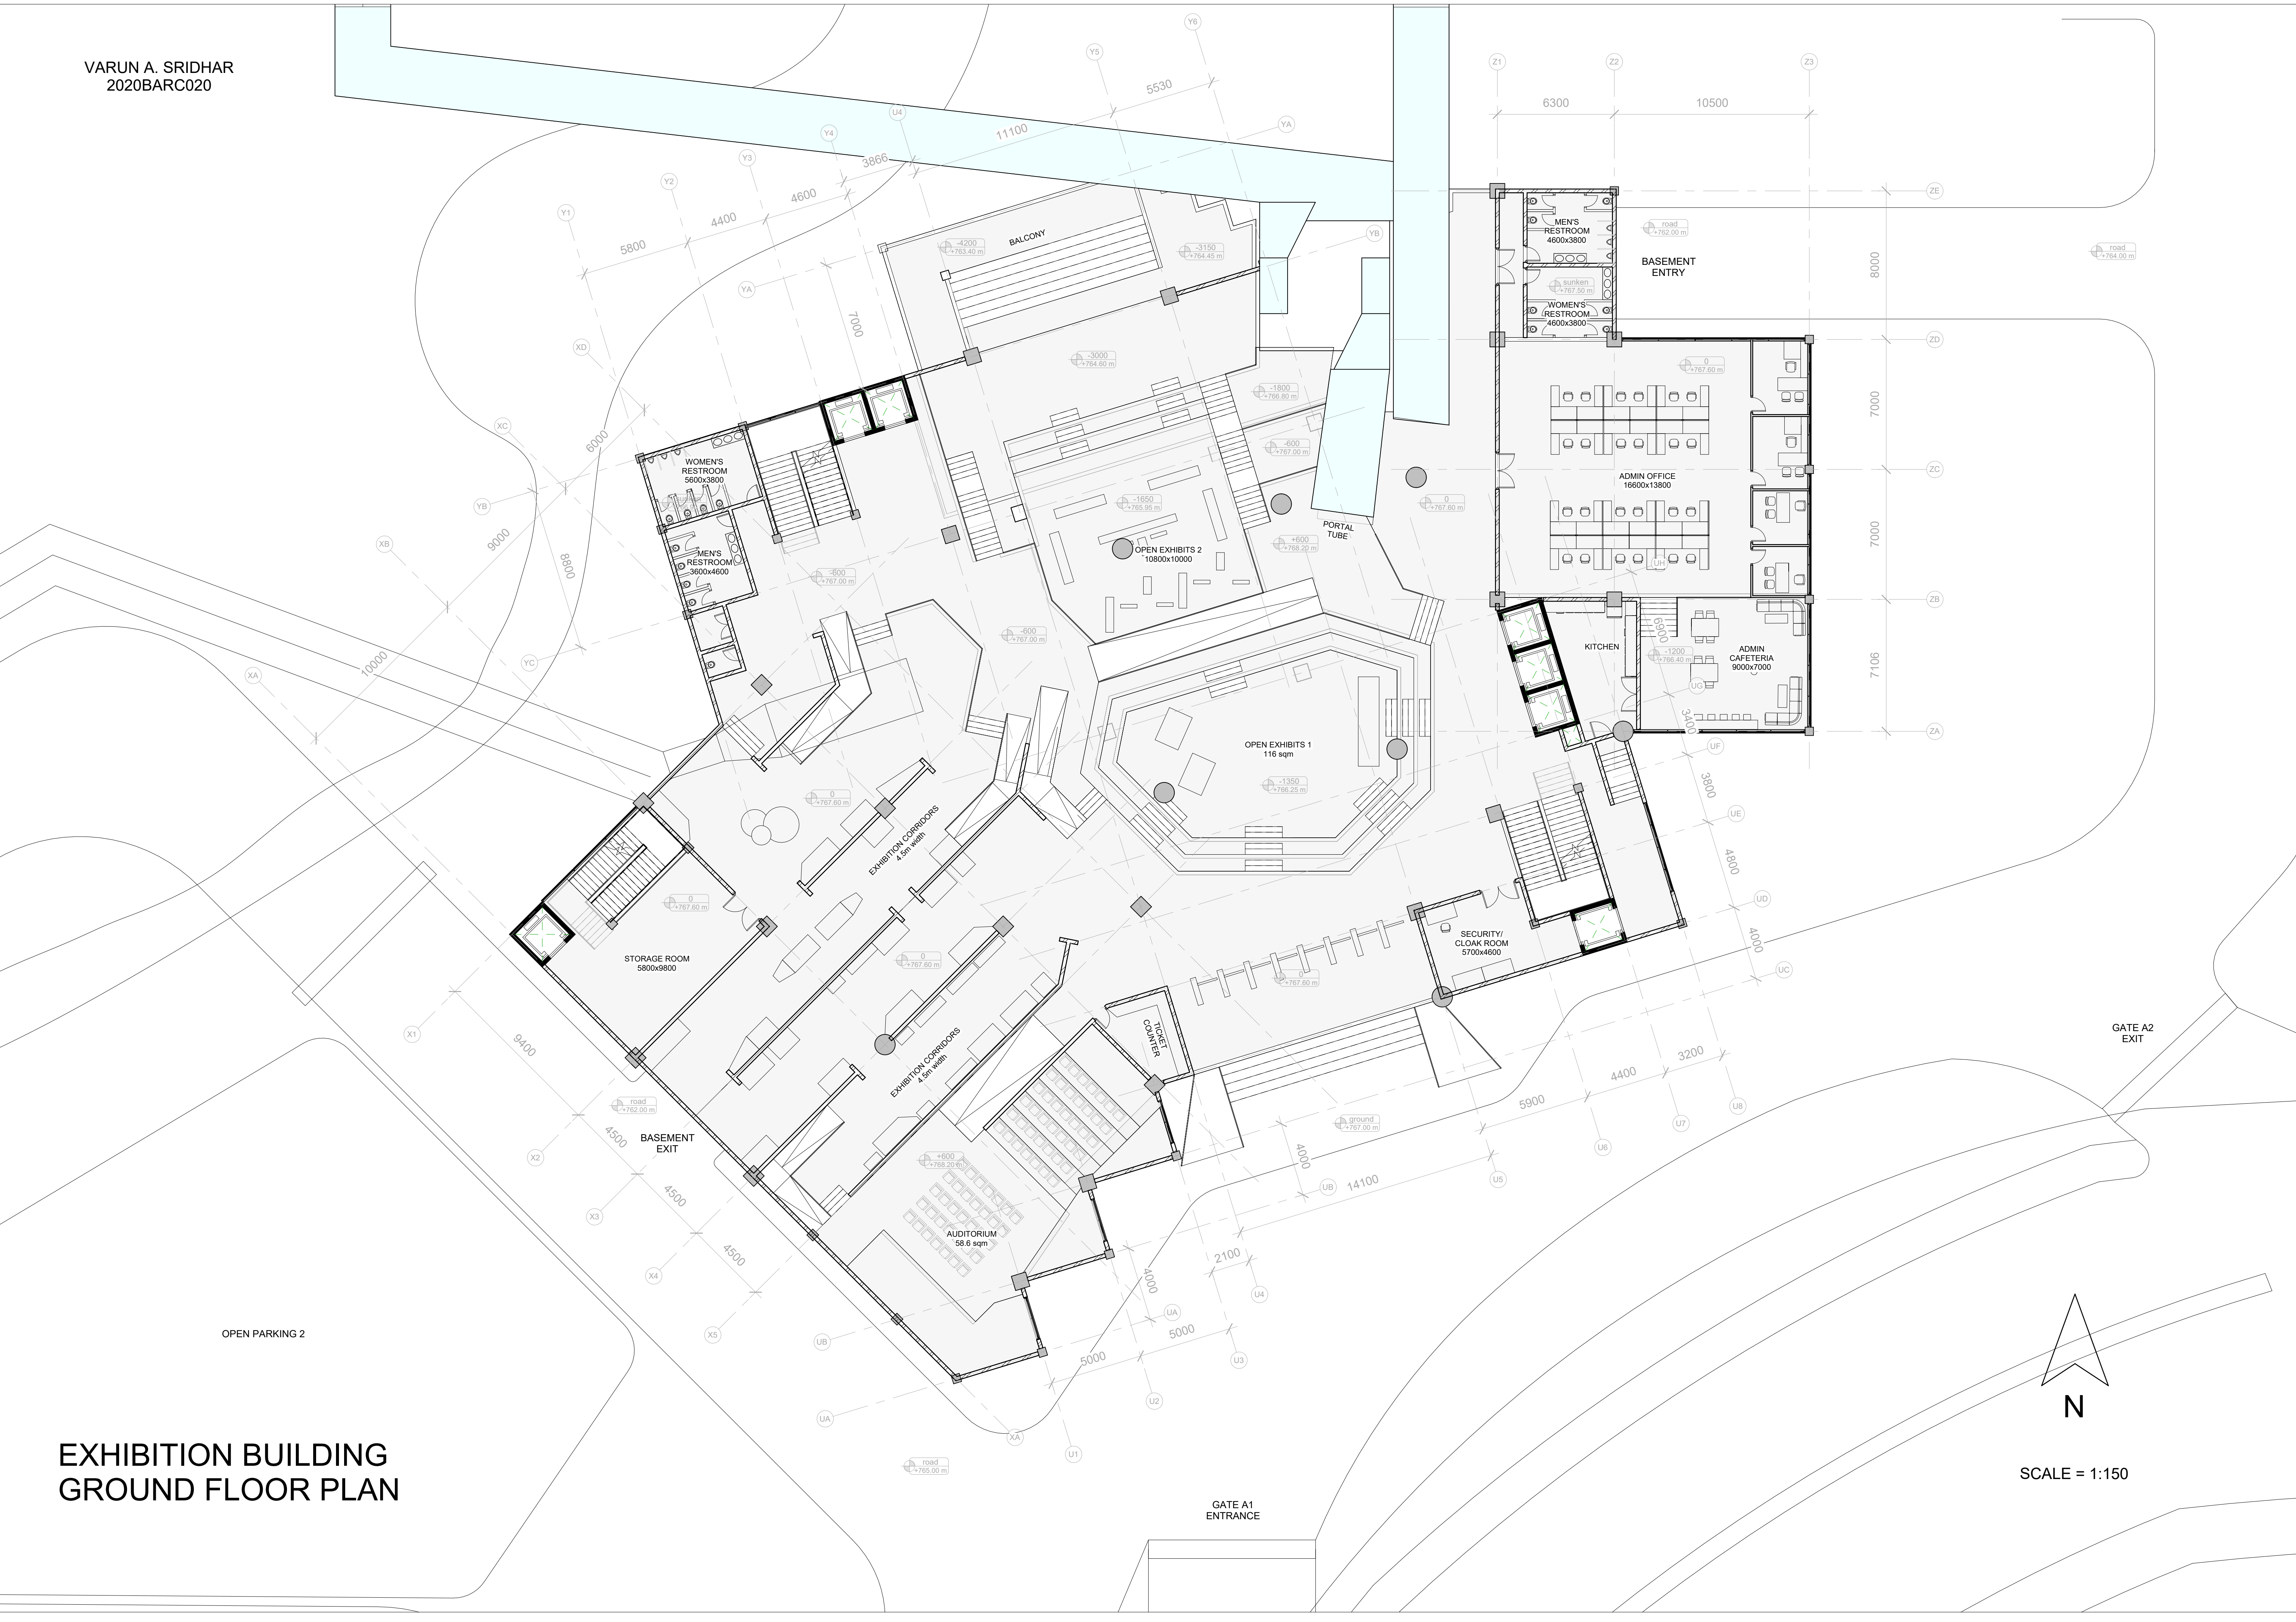




EXHIBITION BUILDING
FIRST FLOOR PLAN

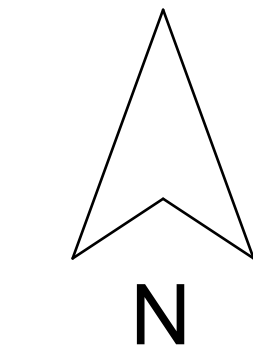


SCALE = 1:150



MANUFACTURING FAB
CLEANROOM - FIRST FLOOR PLAN

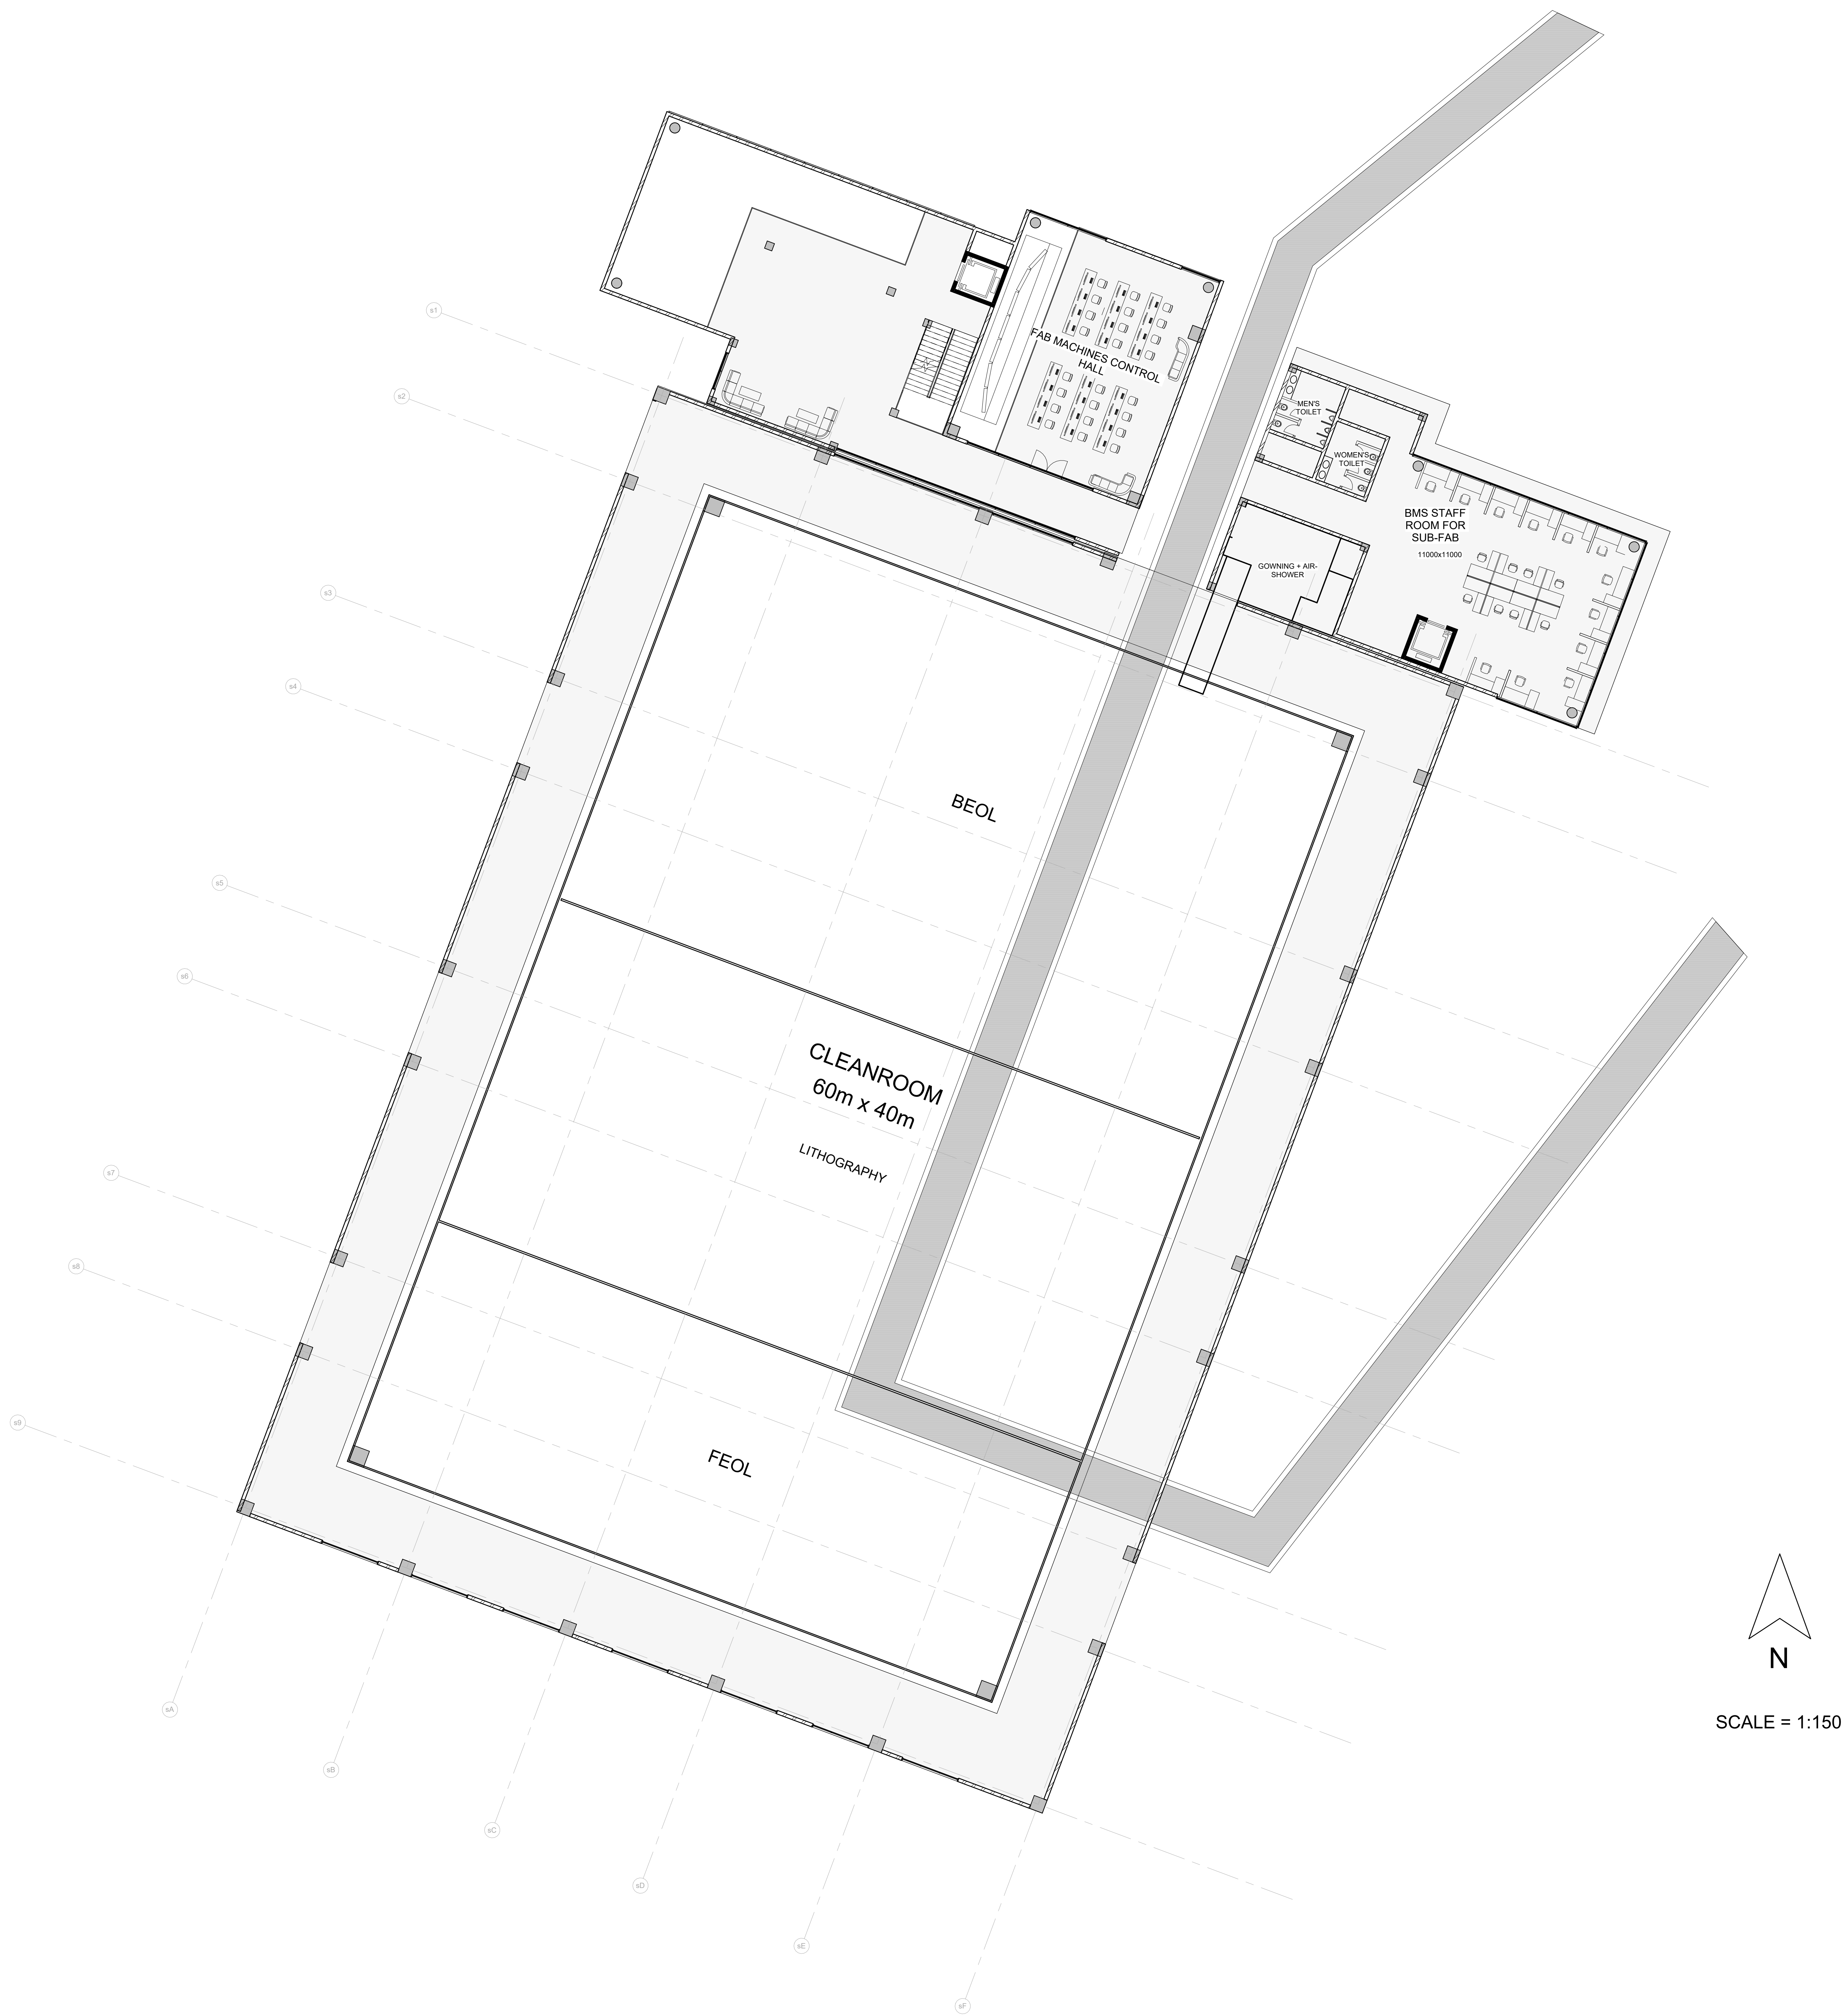

MANUFACTURING FAB
SUB FAB - GROUND FLOOR PLAN

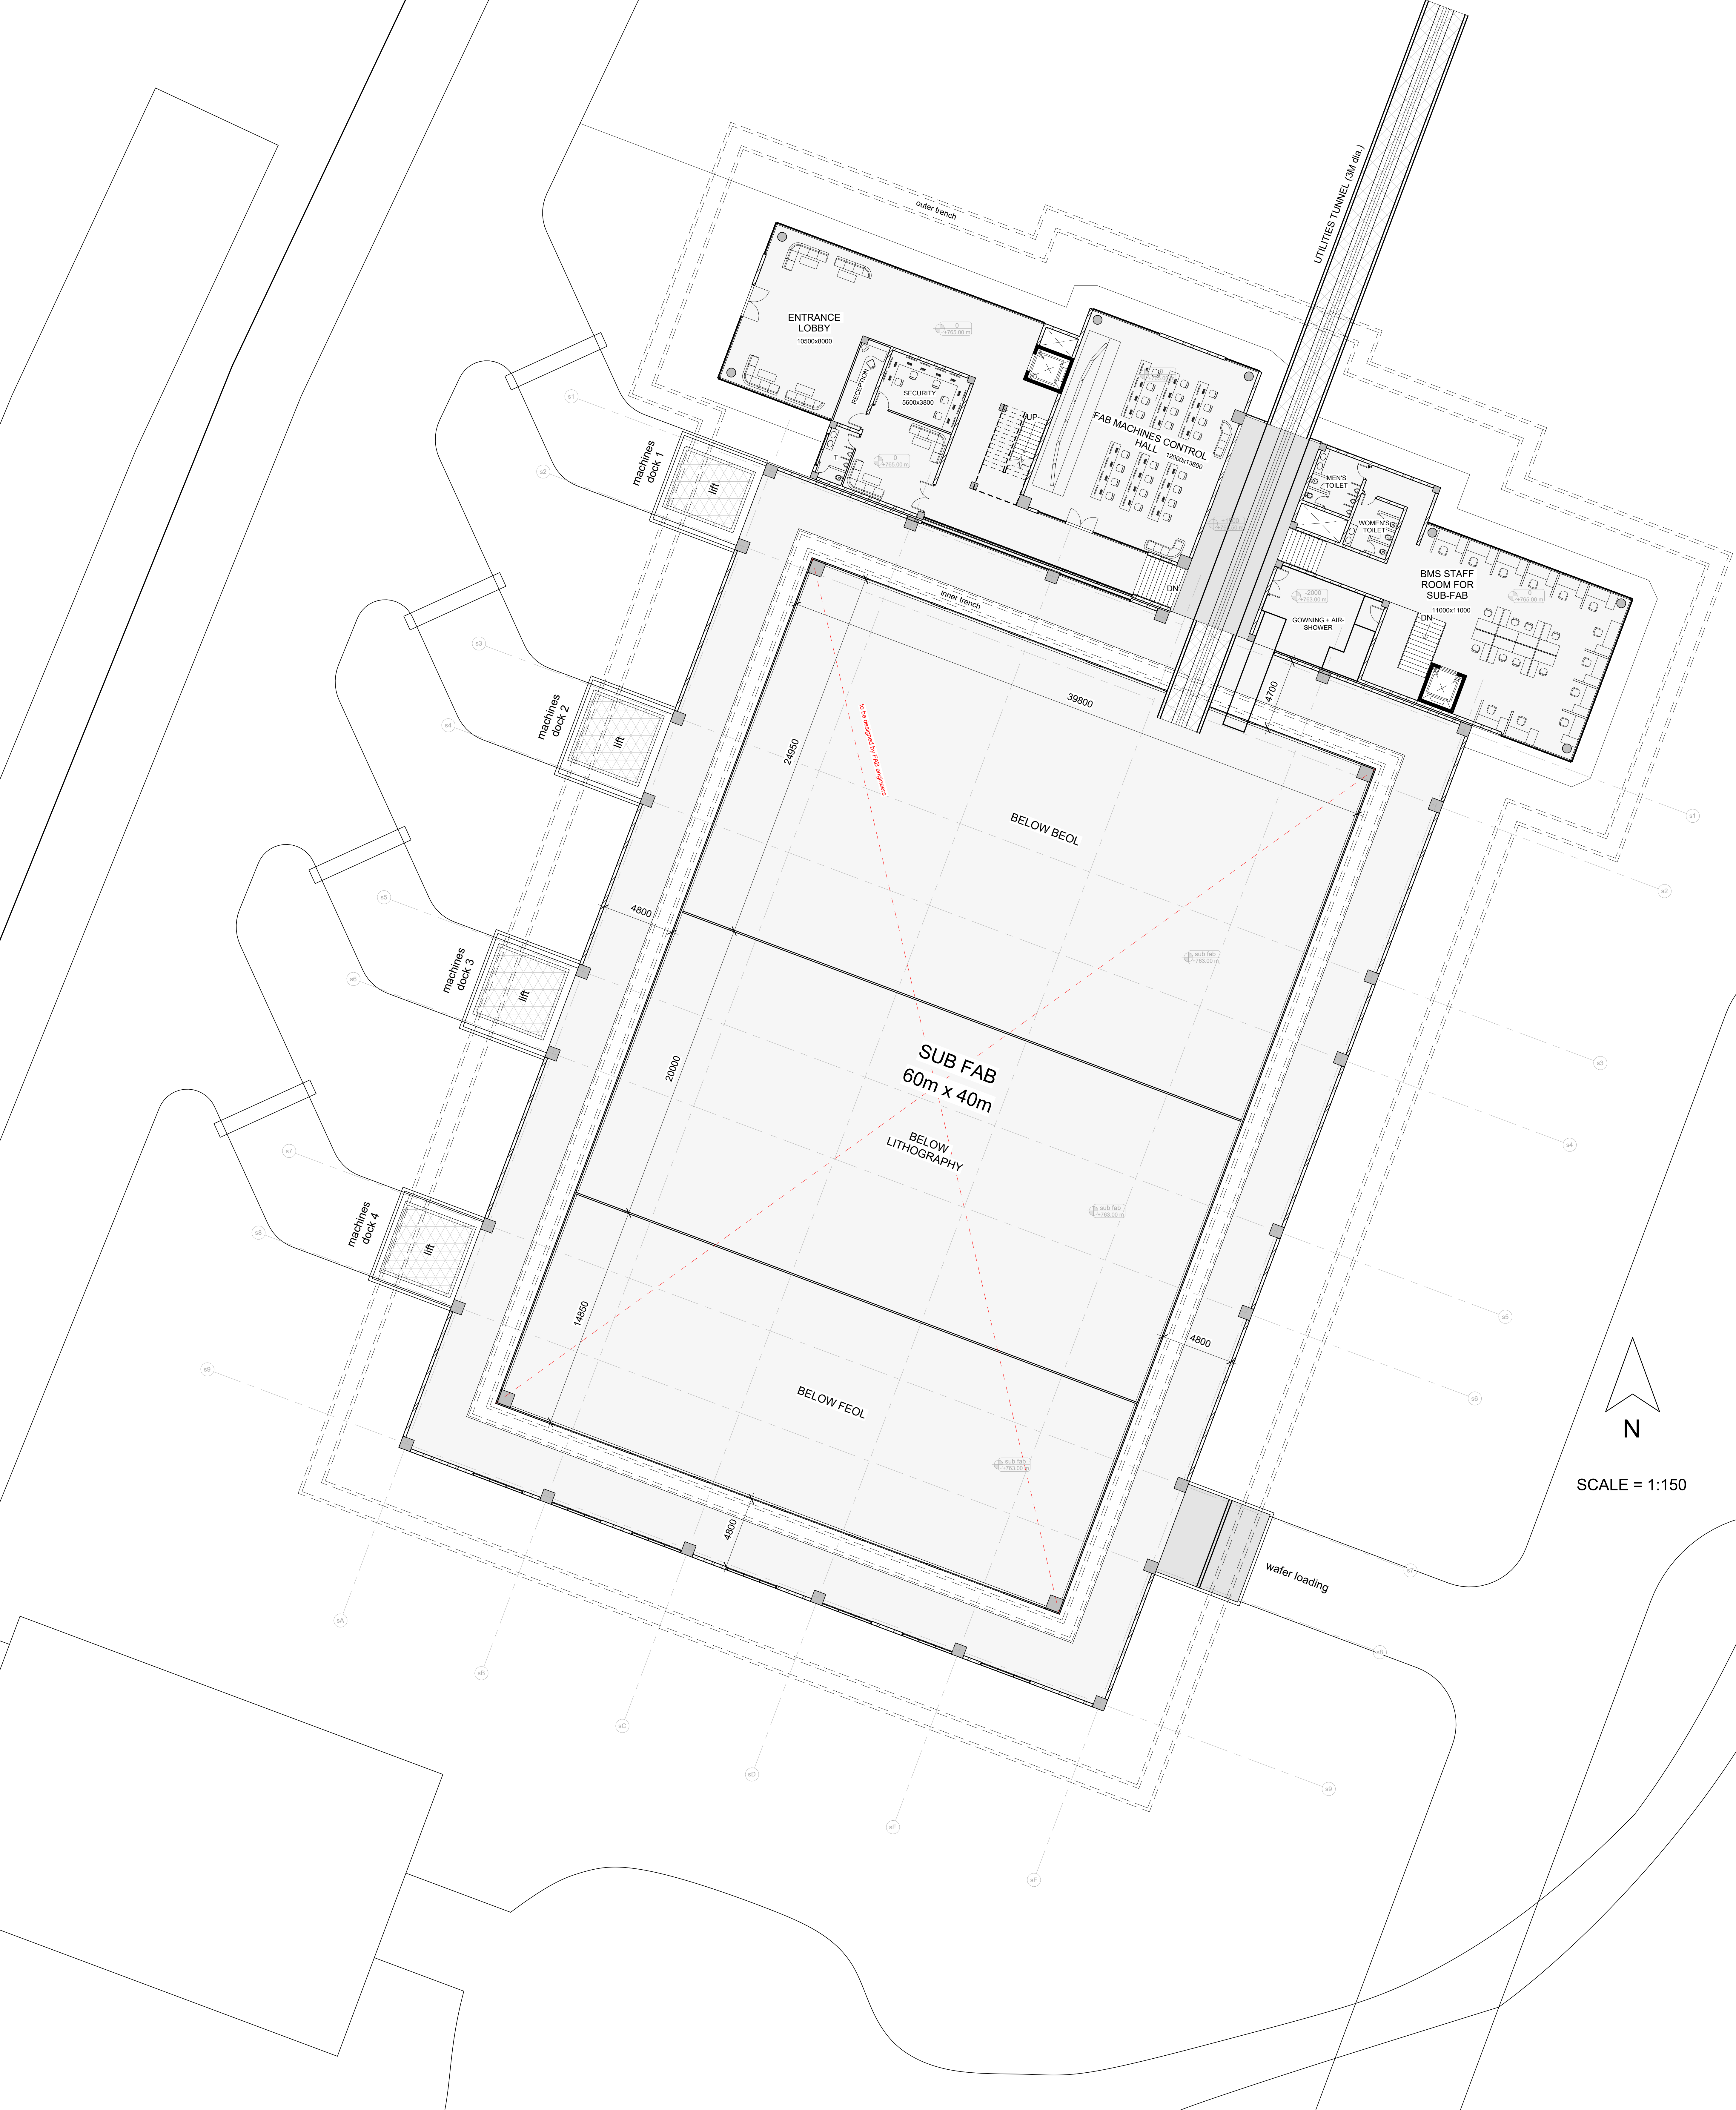

MANUFACTURING FAB GROUND FLOOR PLAN

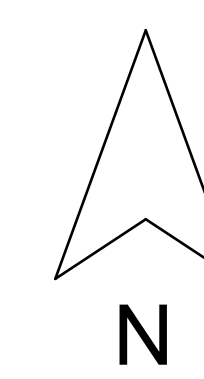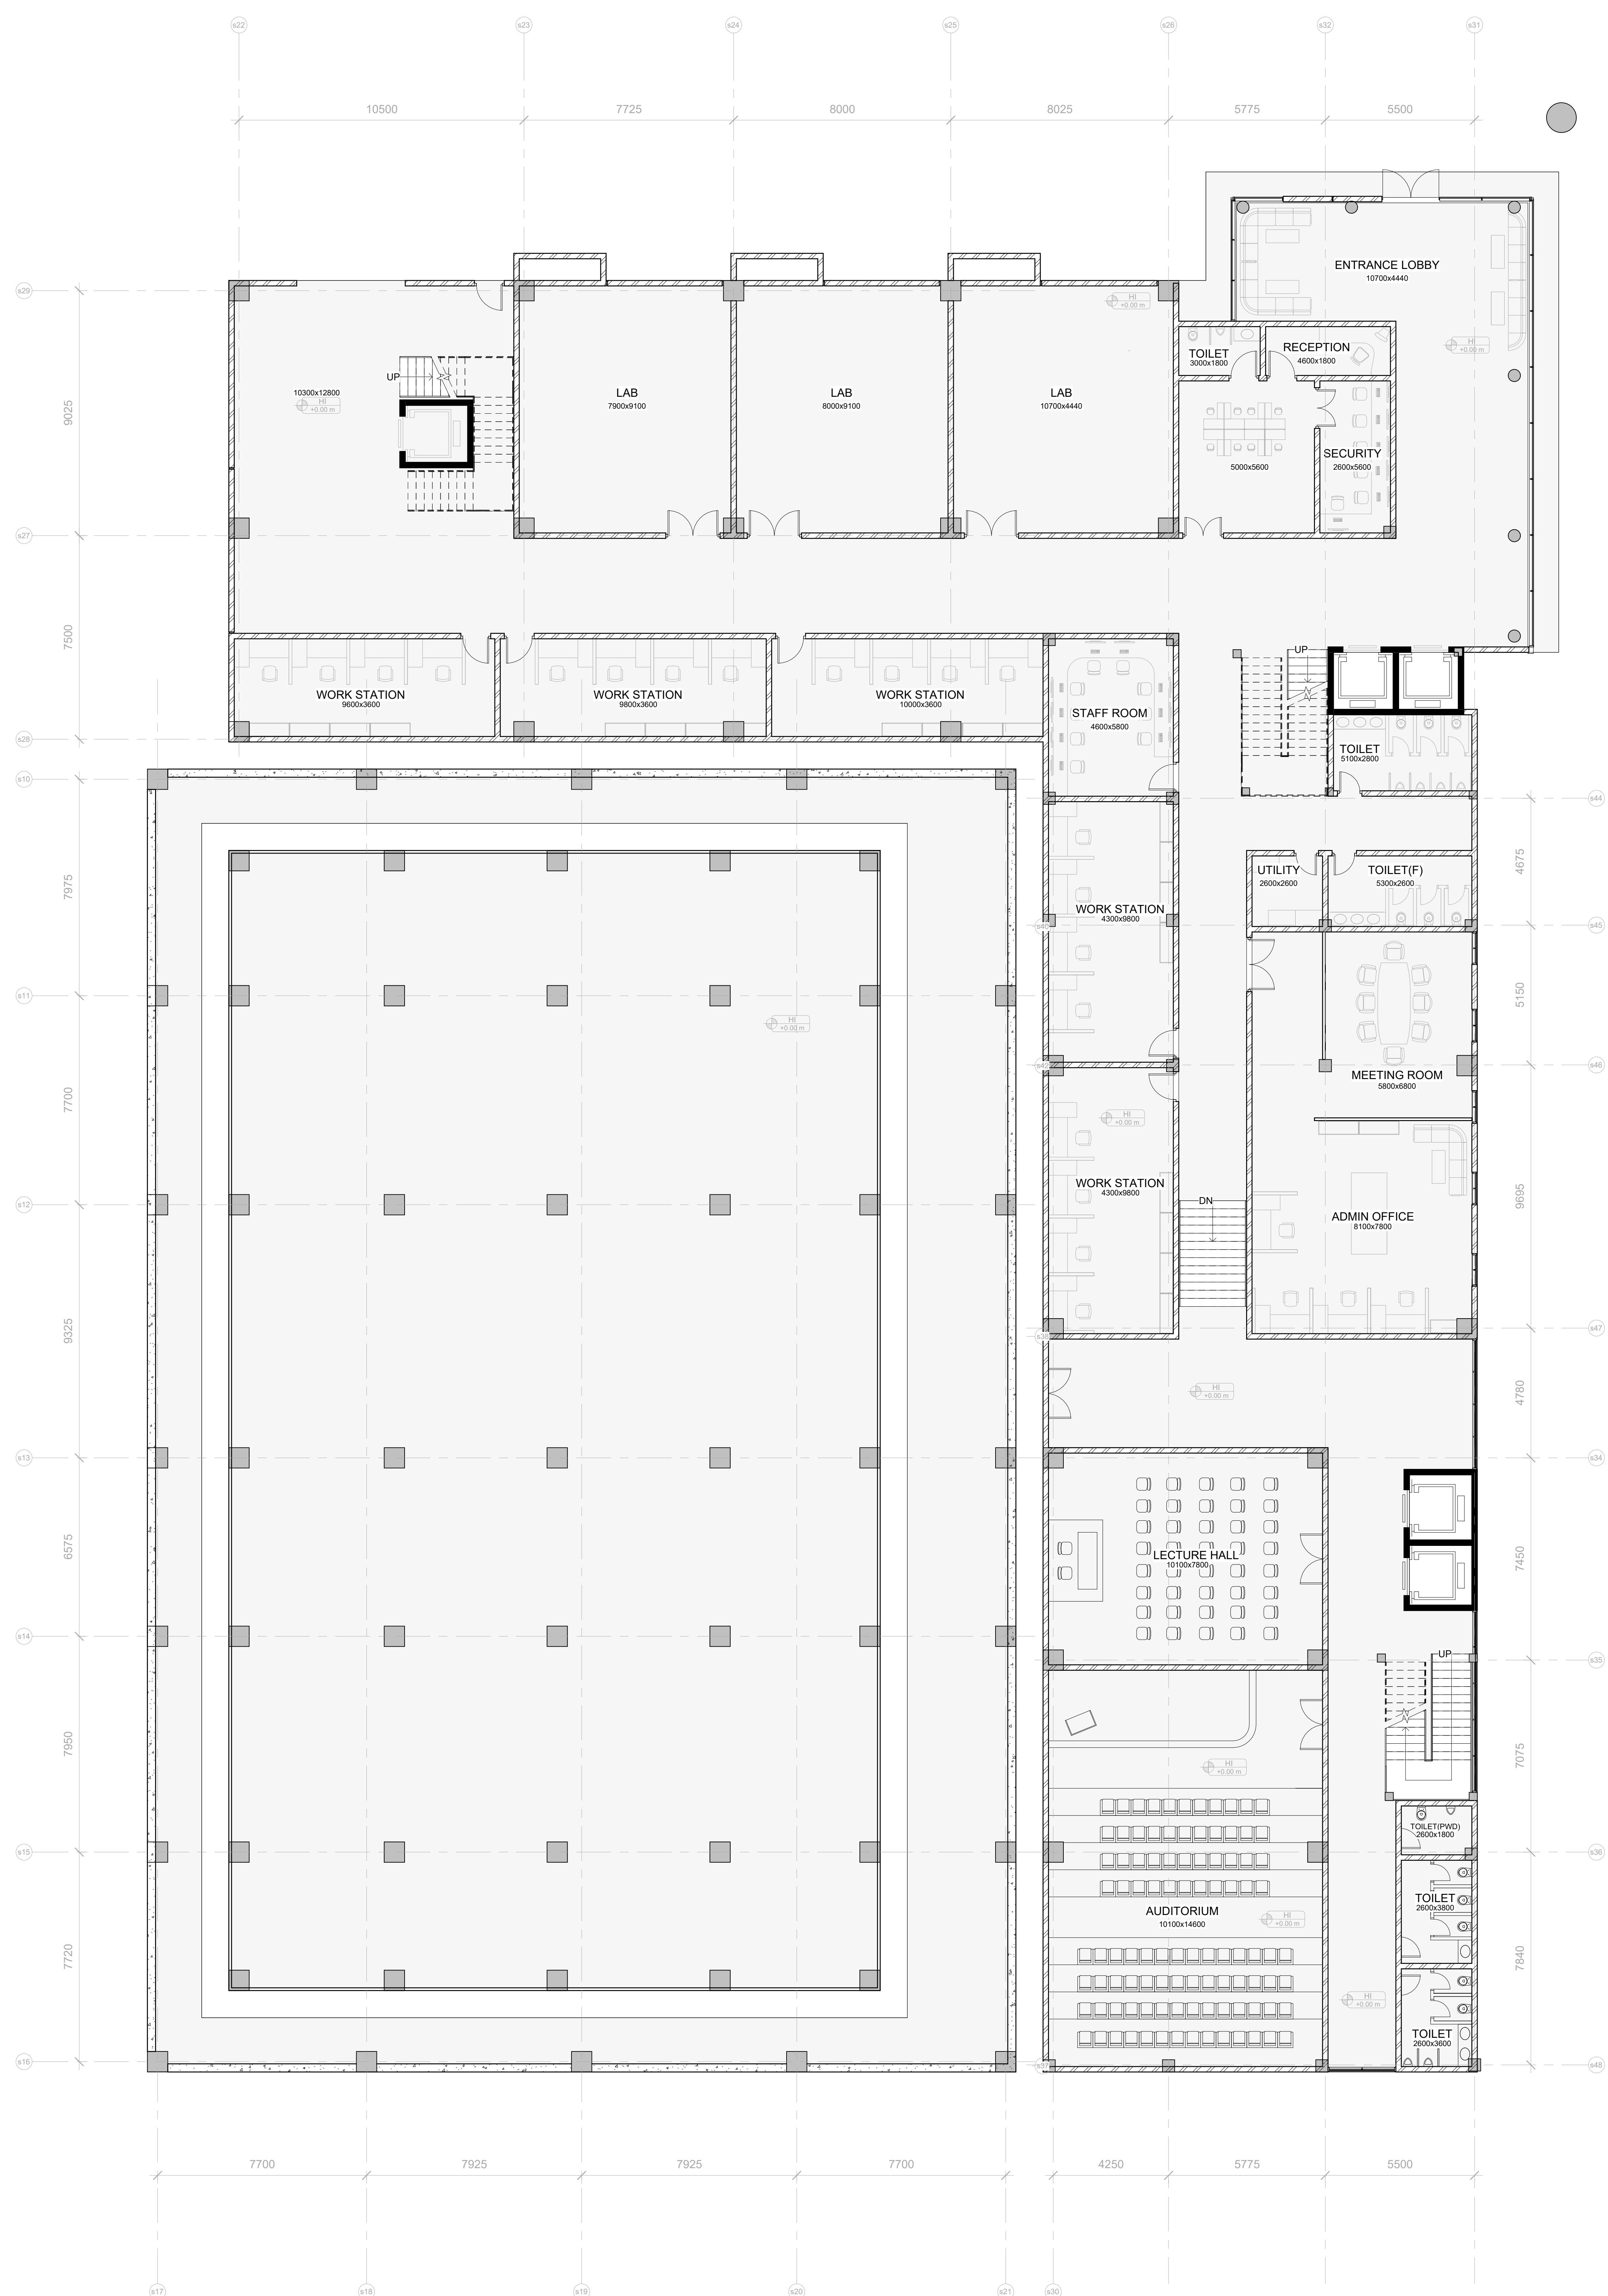

SCALE = 1:100

RESEARCH FAB
FIRST FLOOR PLAN

